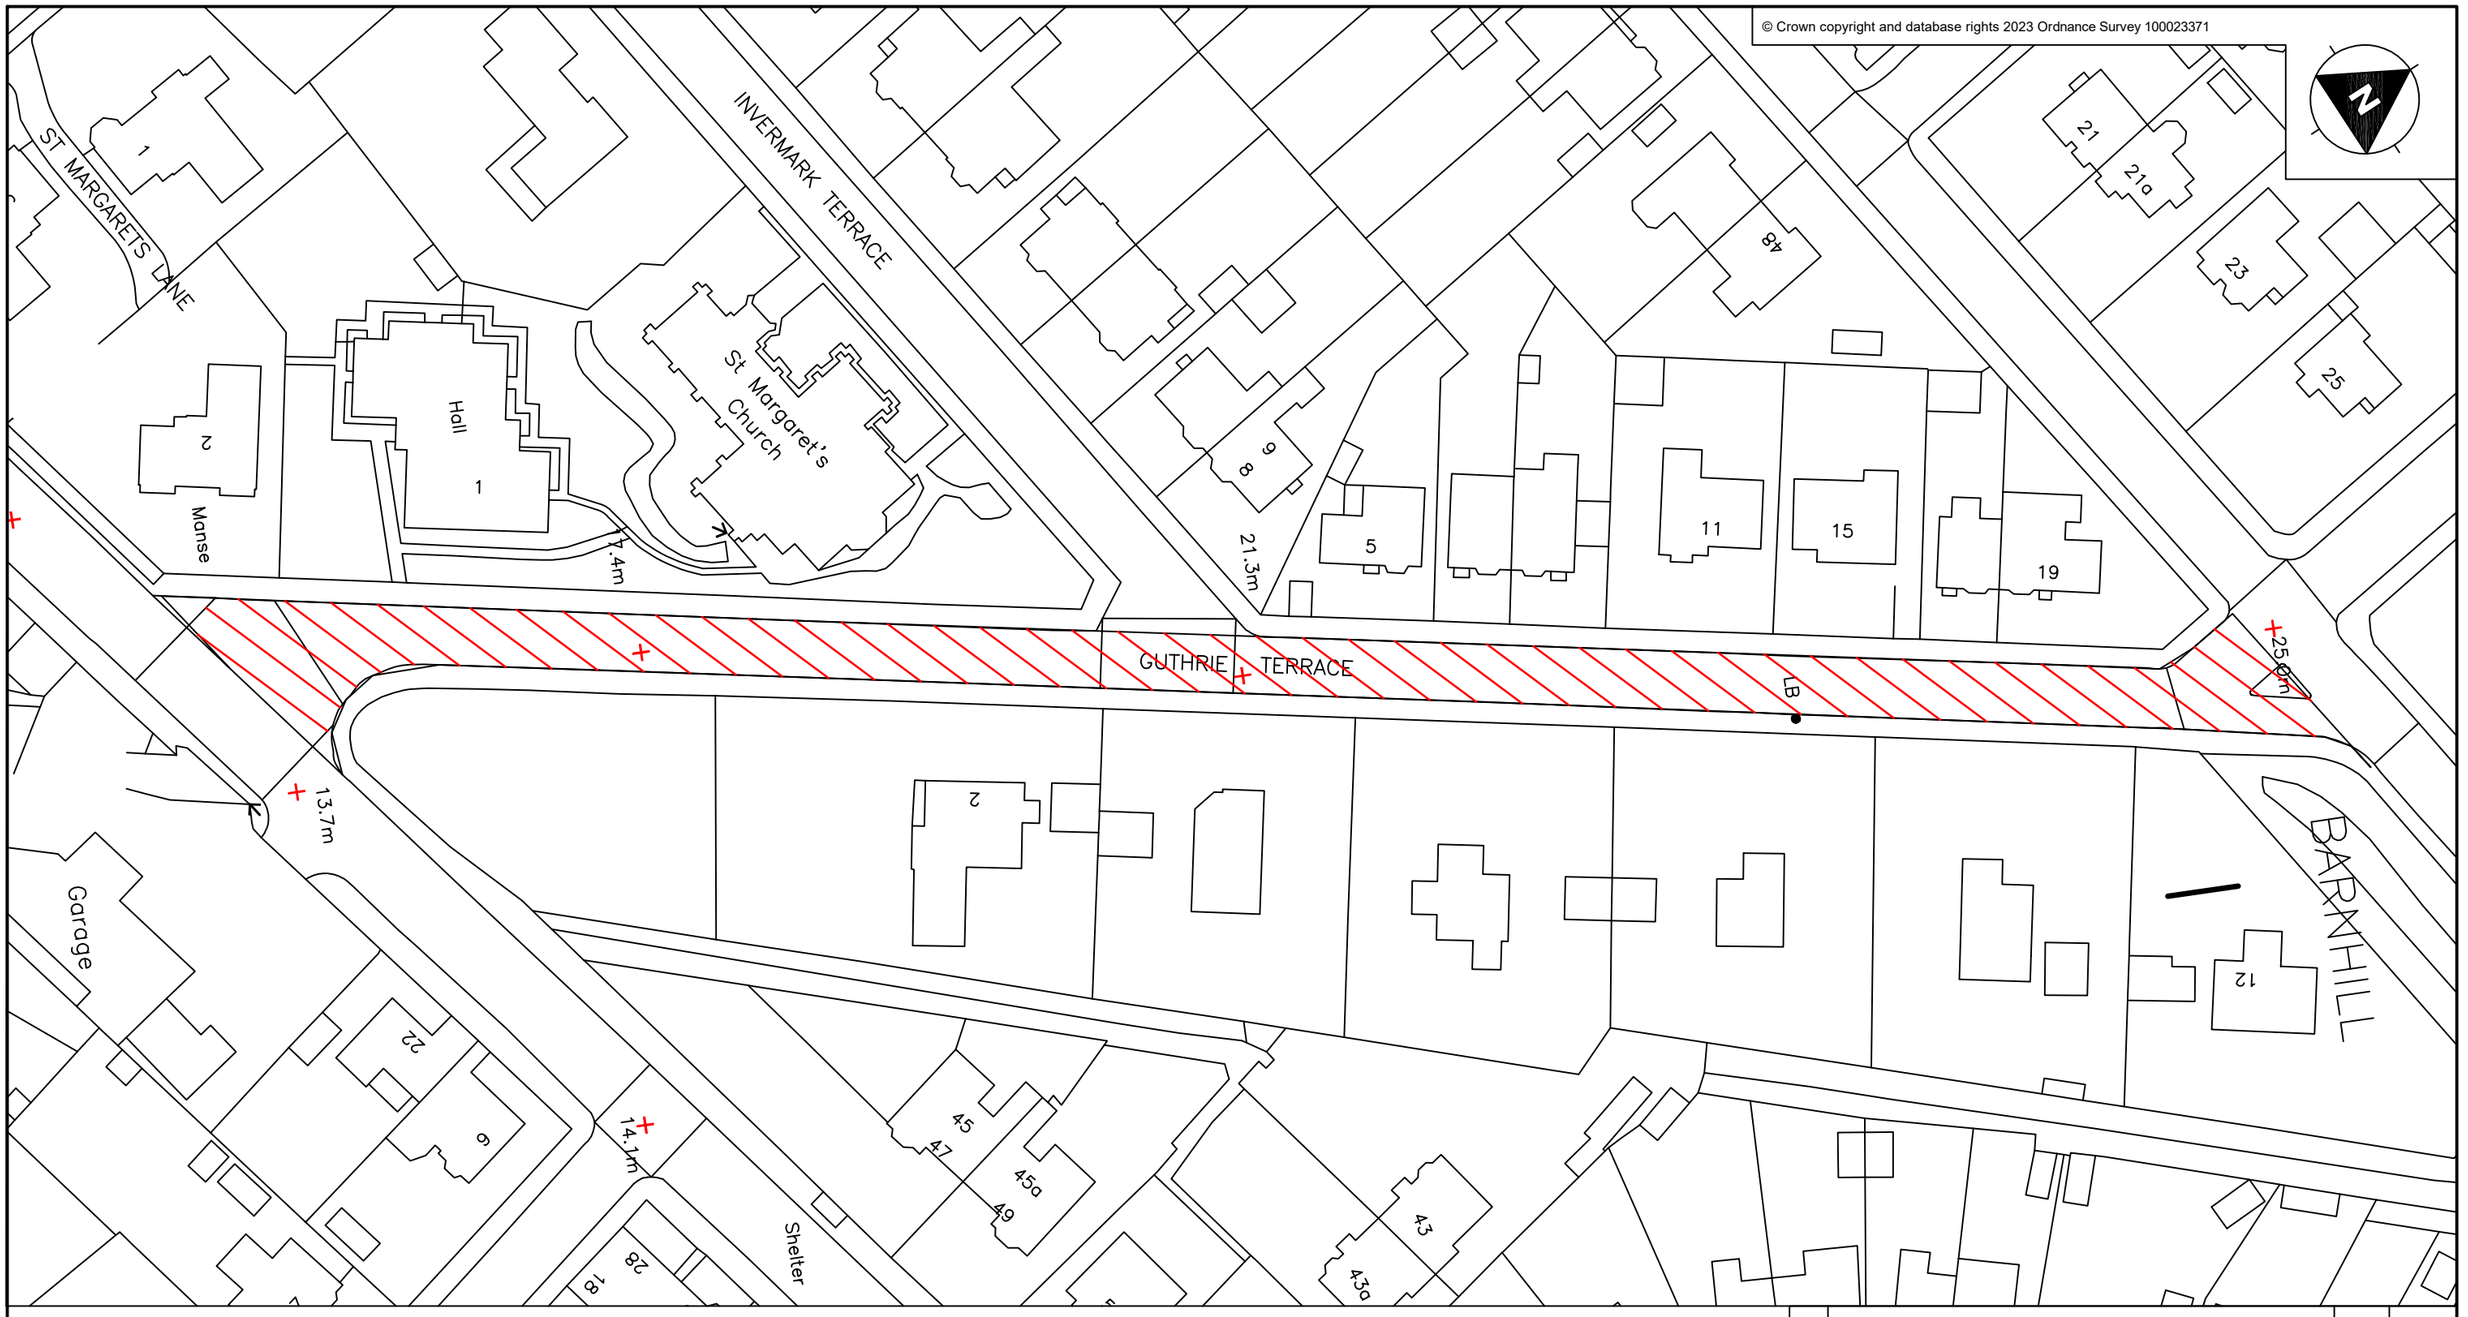

Delivered in 1 Phase of Construction

Taycoat

- 40mm AC 10 100/150 (close graded surface)
- 1920m2
- Screed where required

Note:

- Works shall be protected in accordance with Safety at Street Works and Road Works CoP
- Works to place under complete closure of Guthrie Terrace
- Works to be carried out in phases to minimise disruption to footway users and businesses
- Contractor to ensure pedestrian crossing points are maintained at all times
- Pedestrian access for businesses to be maintained at all times.

Rev	Description	Initials	Date

Dundee City Council

Roads Maintenance Partnership
Sustainable Transport and Roads

Project Title: Guthrie Terrace				
Drawing Title: Resurfacing plan				
Drwg No.: R6xxx-DCC-ZZ-DR-C-001	Suitability:	Revision: R0	Project No./Ref.: R	
Drawn: J Mcallister	Checked: SL	Approved: SL	Scale: NTS	Date: 05/05/26

City Development, Dundee House, 50 North Lindsay Street, Dundee, DD1 1LS. Tel: 01382 434000