


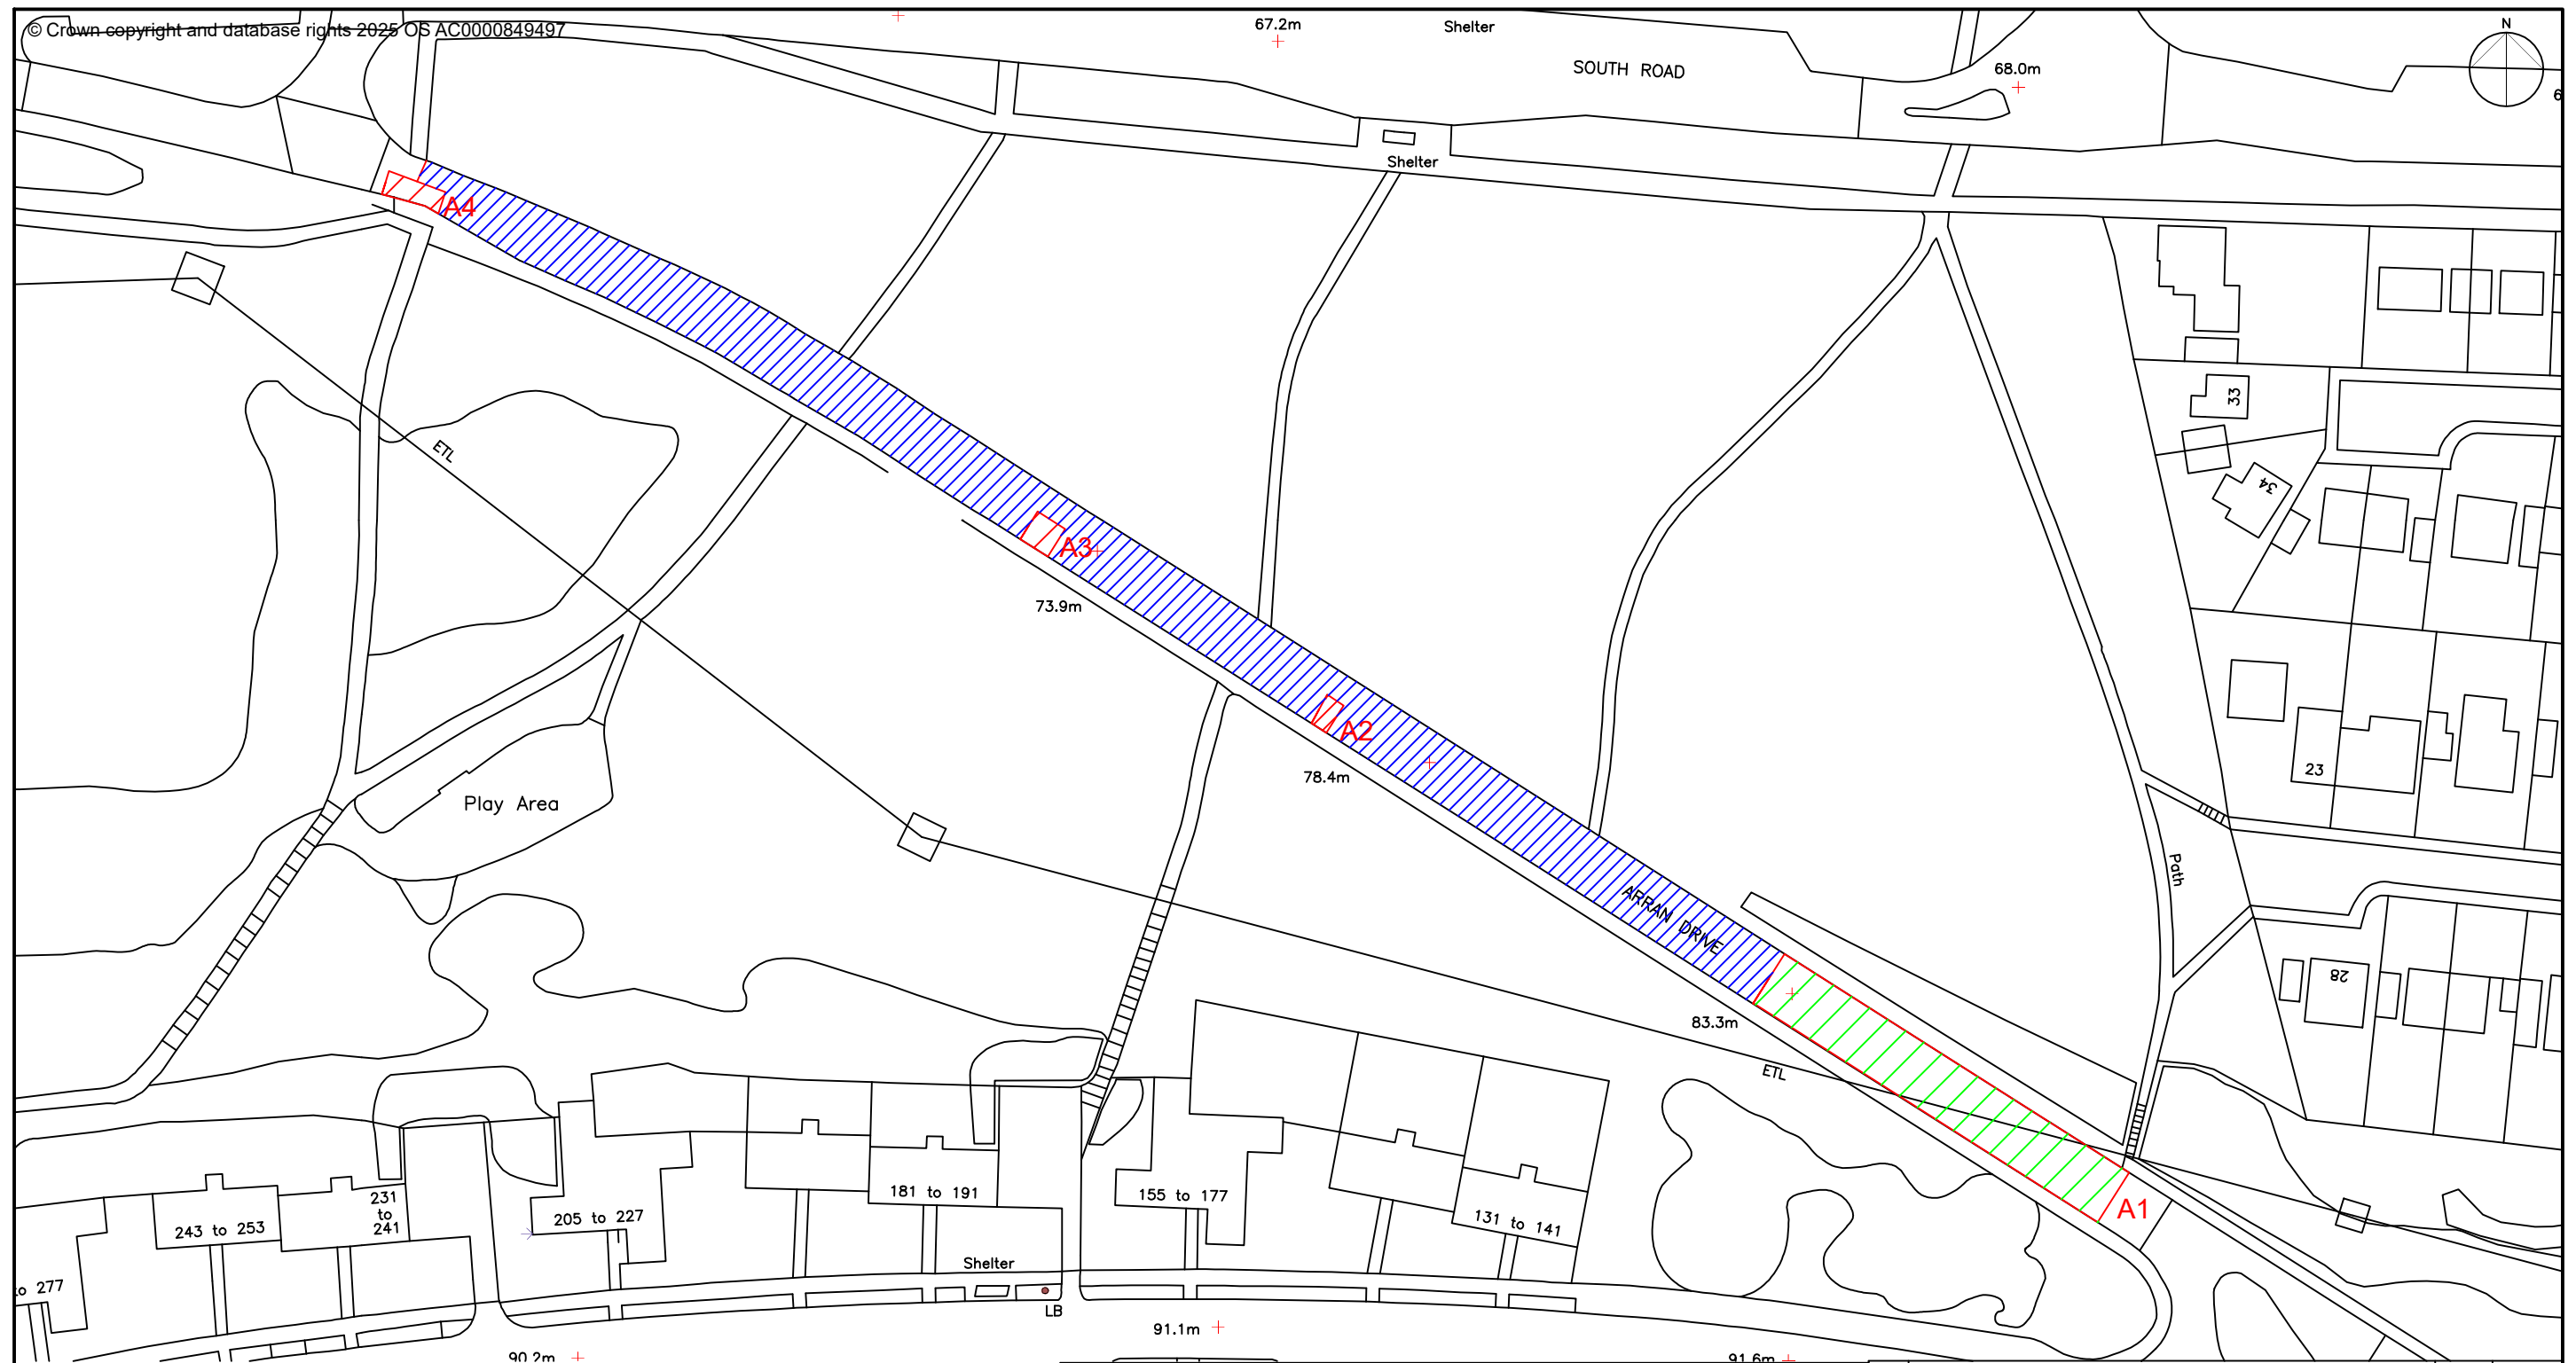

	40mm AC14 Patch - TTL CLOSURES
	100mm AC14 Patch - ROAD CLOSURES
	Surface Dressing - Road closure

PRE PATCHING AREAS		
AREA LABEL	AREA (m ²)	MATERIAL
A1	555	AC14 Surface course, AC 20 Binder
A2	19	
A3	23	
A4	31	

Rev	Description	Initials	Date
	Project Title Arran Drive		
	Drawing Title SD & Patching		
	Dwg No. DCC-SD-001	Suitability S01	Revision R0
	Drawn JMCA	Checked	Approved
		Scale NTS	Date 07/04/26

Roads Maintenance Partnership
Sustainable Transport and Roads

City Development, Dundee House, 50 North Lindsay Street, Dundee, DD1 1LS. Tel: 01382 434000